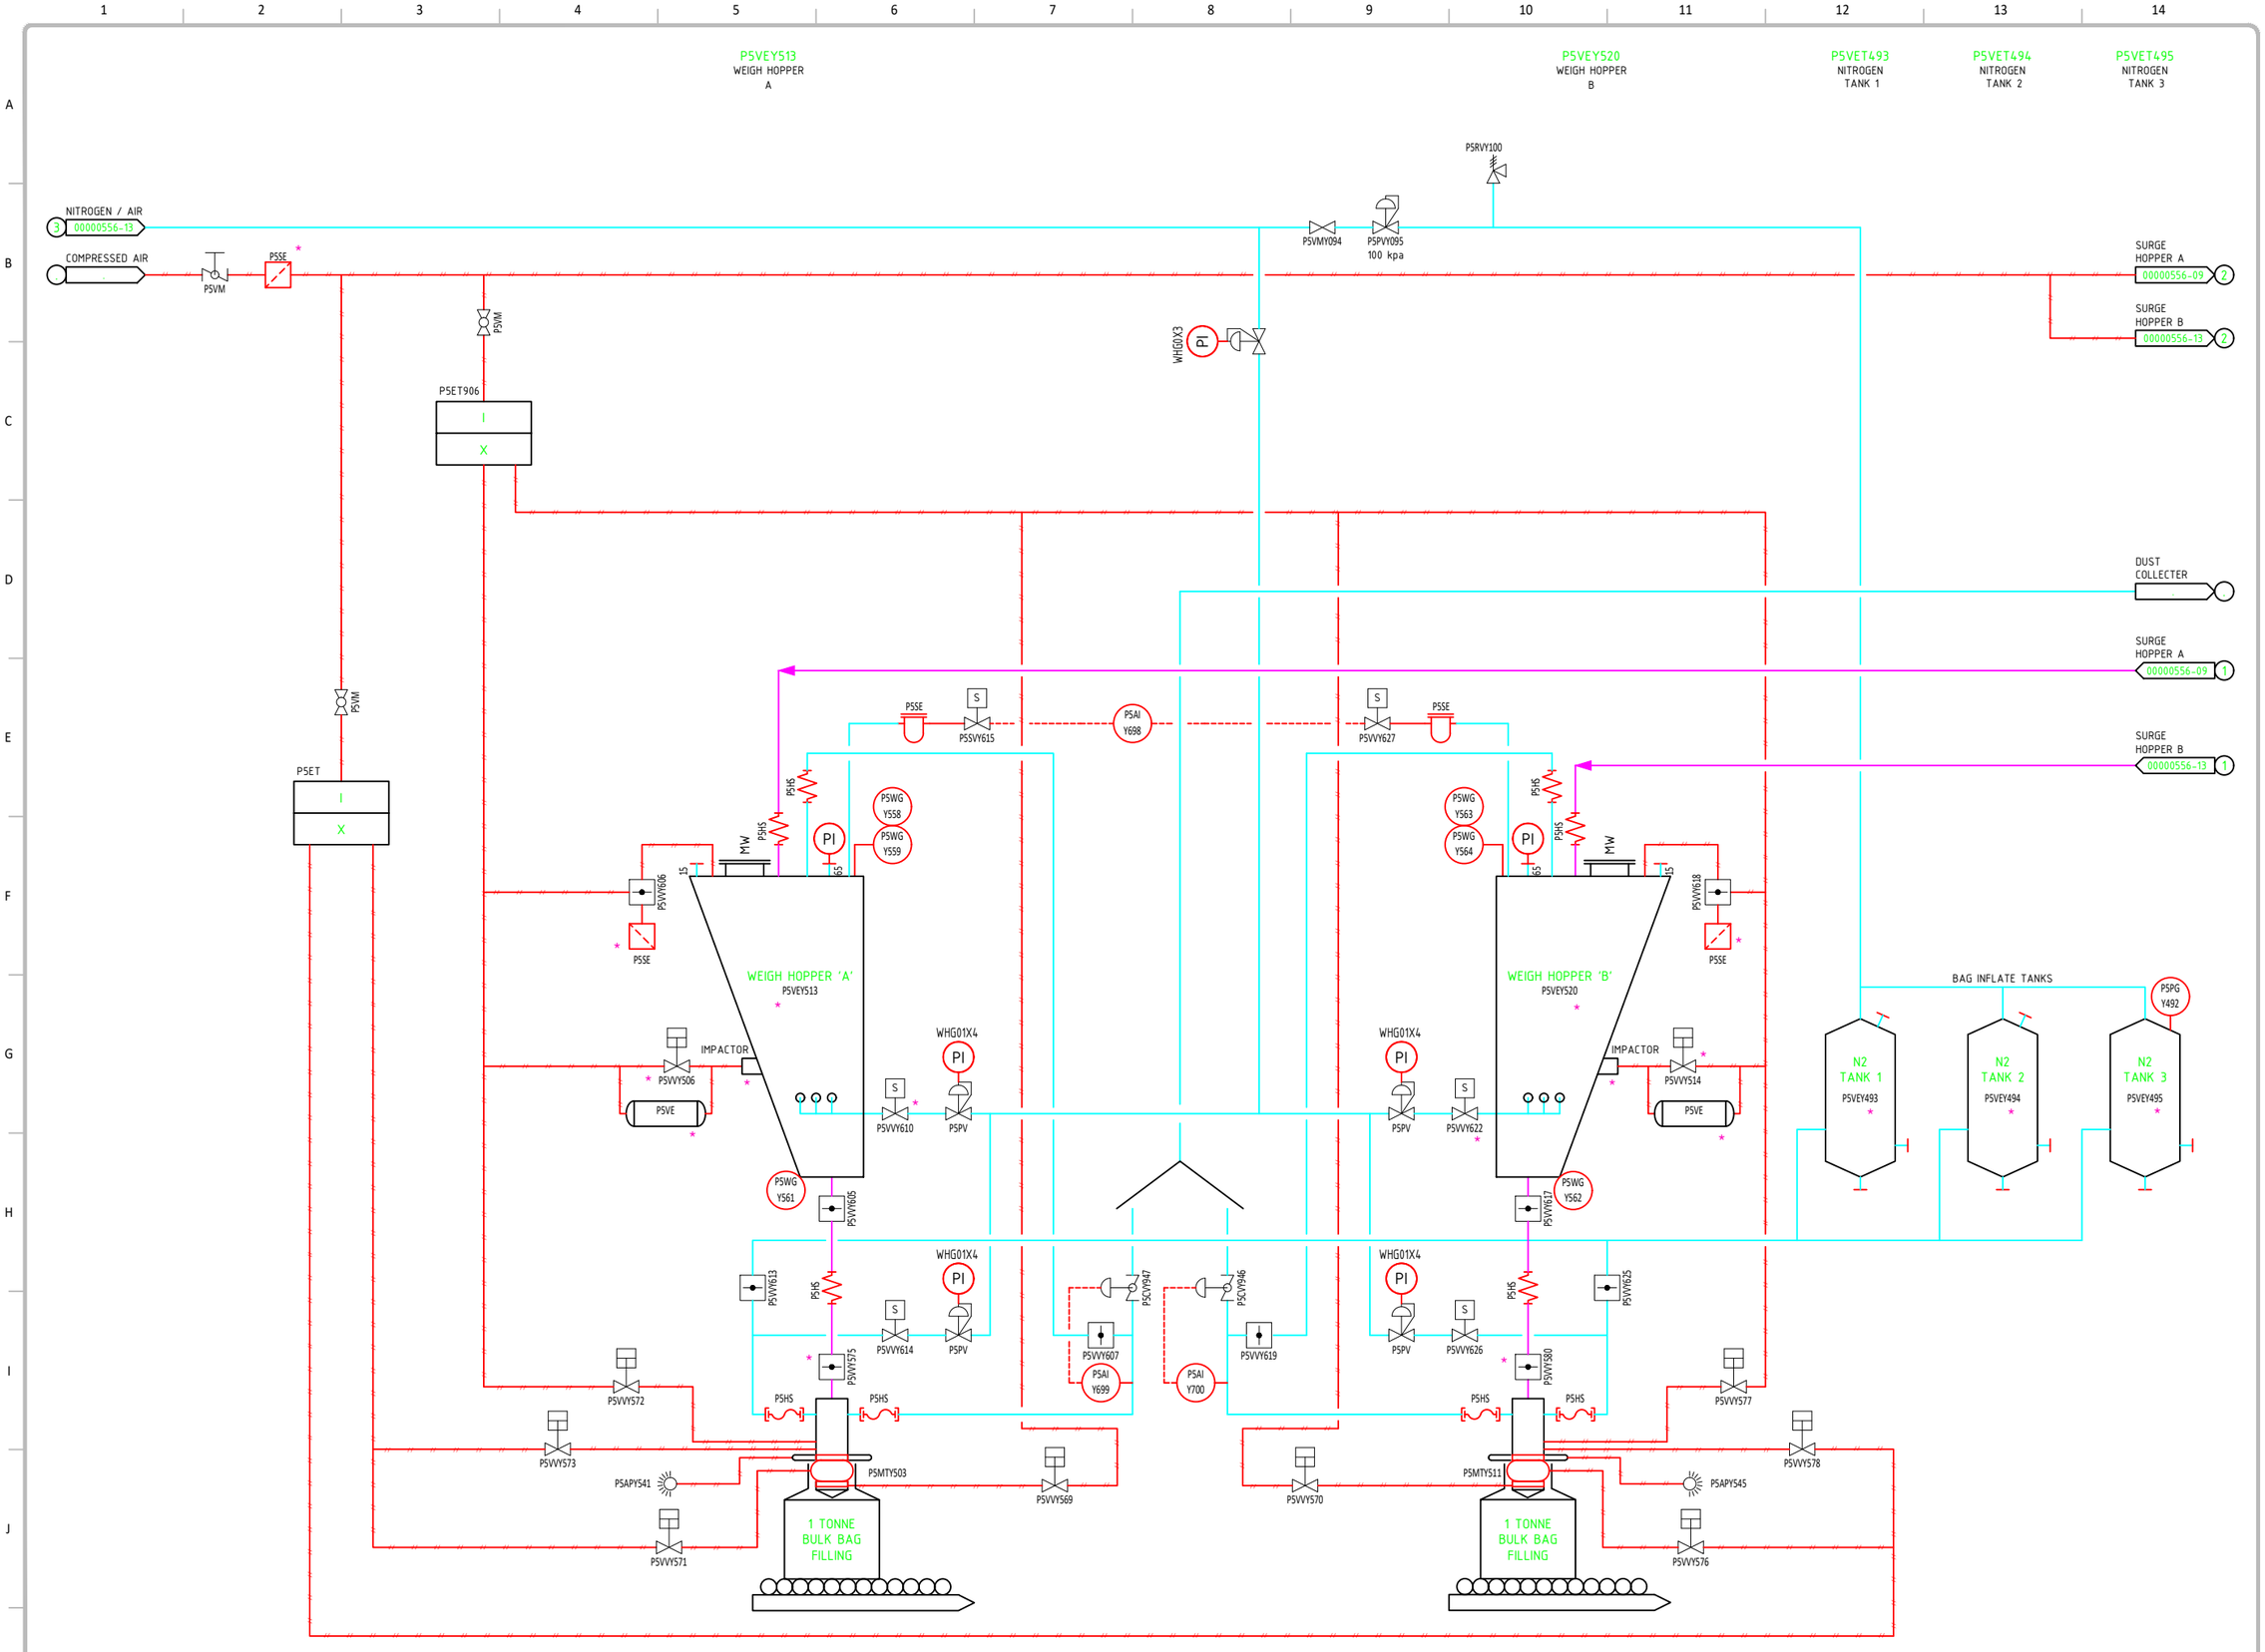

A1

NOTES:

* METAL MAPPING
POTENTIAL CONTAMINATION POINT

REFERENCE DRAWINGS	
	FONTERRA PIPING/MECHANICAL LEGEND SHEETS
	FONTERRA P&ID LEGEND SHEETS

4	ISSUED - Mohamed.Chaar@tetrapak.com	SAC	11.06.2024
3	AS BUILT - Mohamed.Chaar@tetrapak.com	SAC	10.04.2024
2	ISSUED - Henri.Viljoen@tetrapak.com	SAC	21.11.2023
F	FORMAT UPDATE	SAC	26.11.2021
E	TAG UPDATES & METAL MAPPING	HM	09.06.2016
D	UPDATES - NEIL CLOUGH	SAC	26.11.2015
C	UPDATES - NEIL CLOUGH	SAC	18.08.2015
B	SAPHT UPDATE/TITLE	SAR	12.08.2010
-			

REVISIONS

DO NOT SCALE
REPORT ALL ERRORS

.\Fonterra_rgb_std_L.PNG

DELETED THIS BLOCK AND
ADD YOUR COMPANY
LOGO HERE

COPYRIGHT:
THIS DRAWING IS THE EXCLUSIVE PROPERTY OF FONTERRA. IT MUST NOT BE COPIED BY ANY MEANS, WITHOUT THE WRITTEN CONSENT OF FONTERRA DRAWING CONTROL.

Drawn: L.KLENNER
Date: 16.07.2002
Checked:
Scale: NTS

Title.
WHAREROA POWDER 5
WEIGH HOPPERS A & B
BULK PACKERS
P&ID

Dwg No. 00000556 - 15
Rev 4

SITE	PLANT	DISCIPLINE	TYPE
WH	P5	PI	S